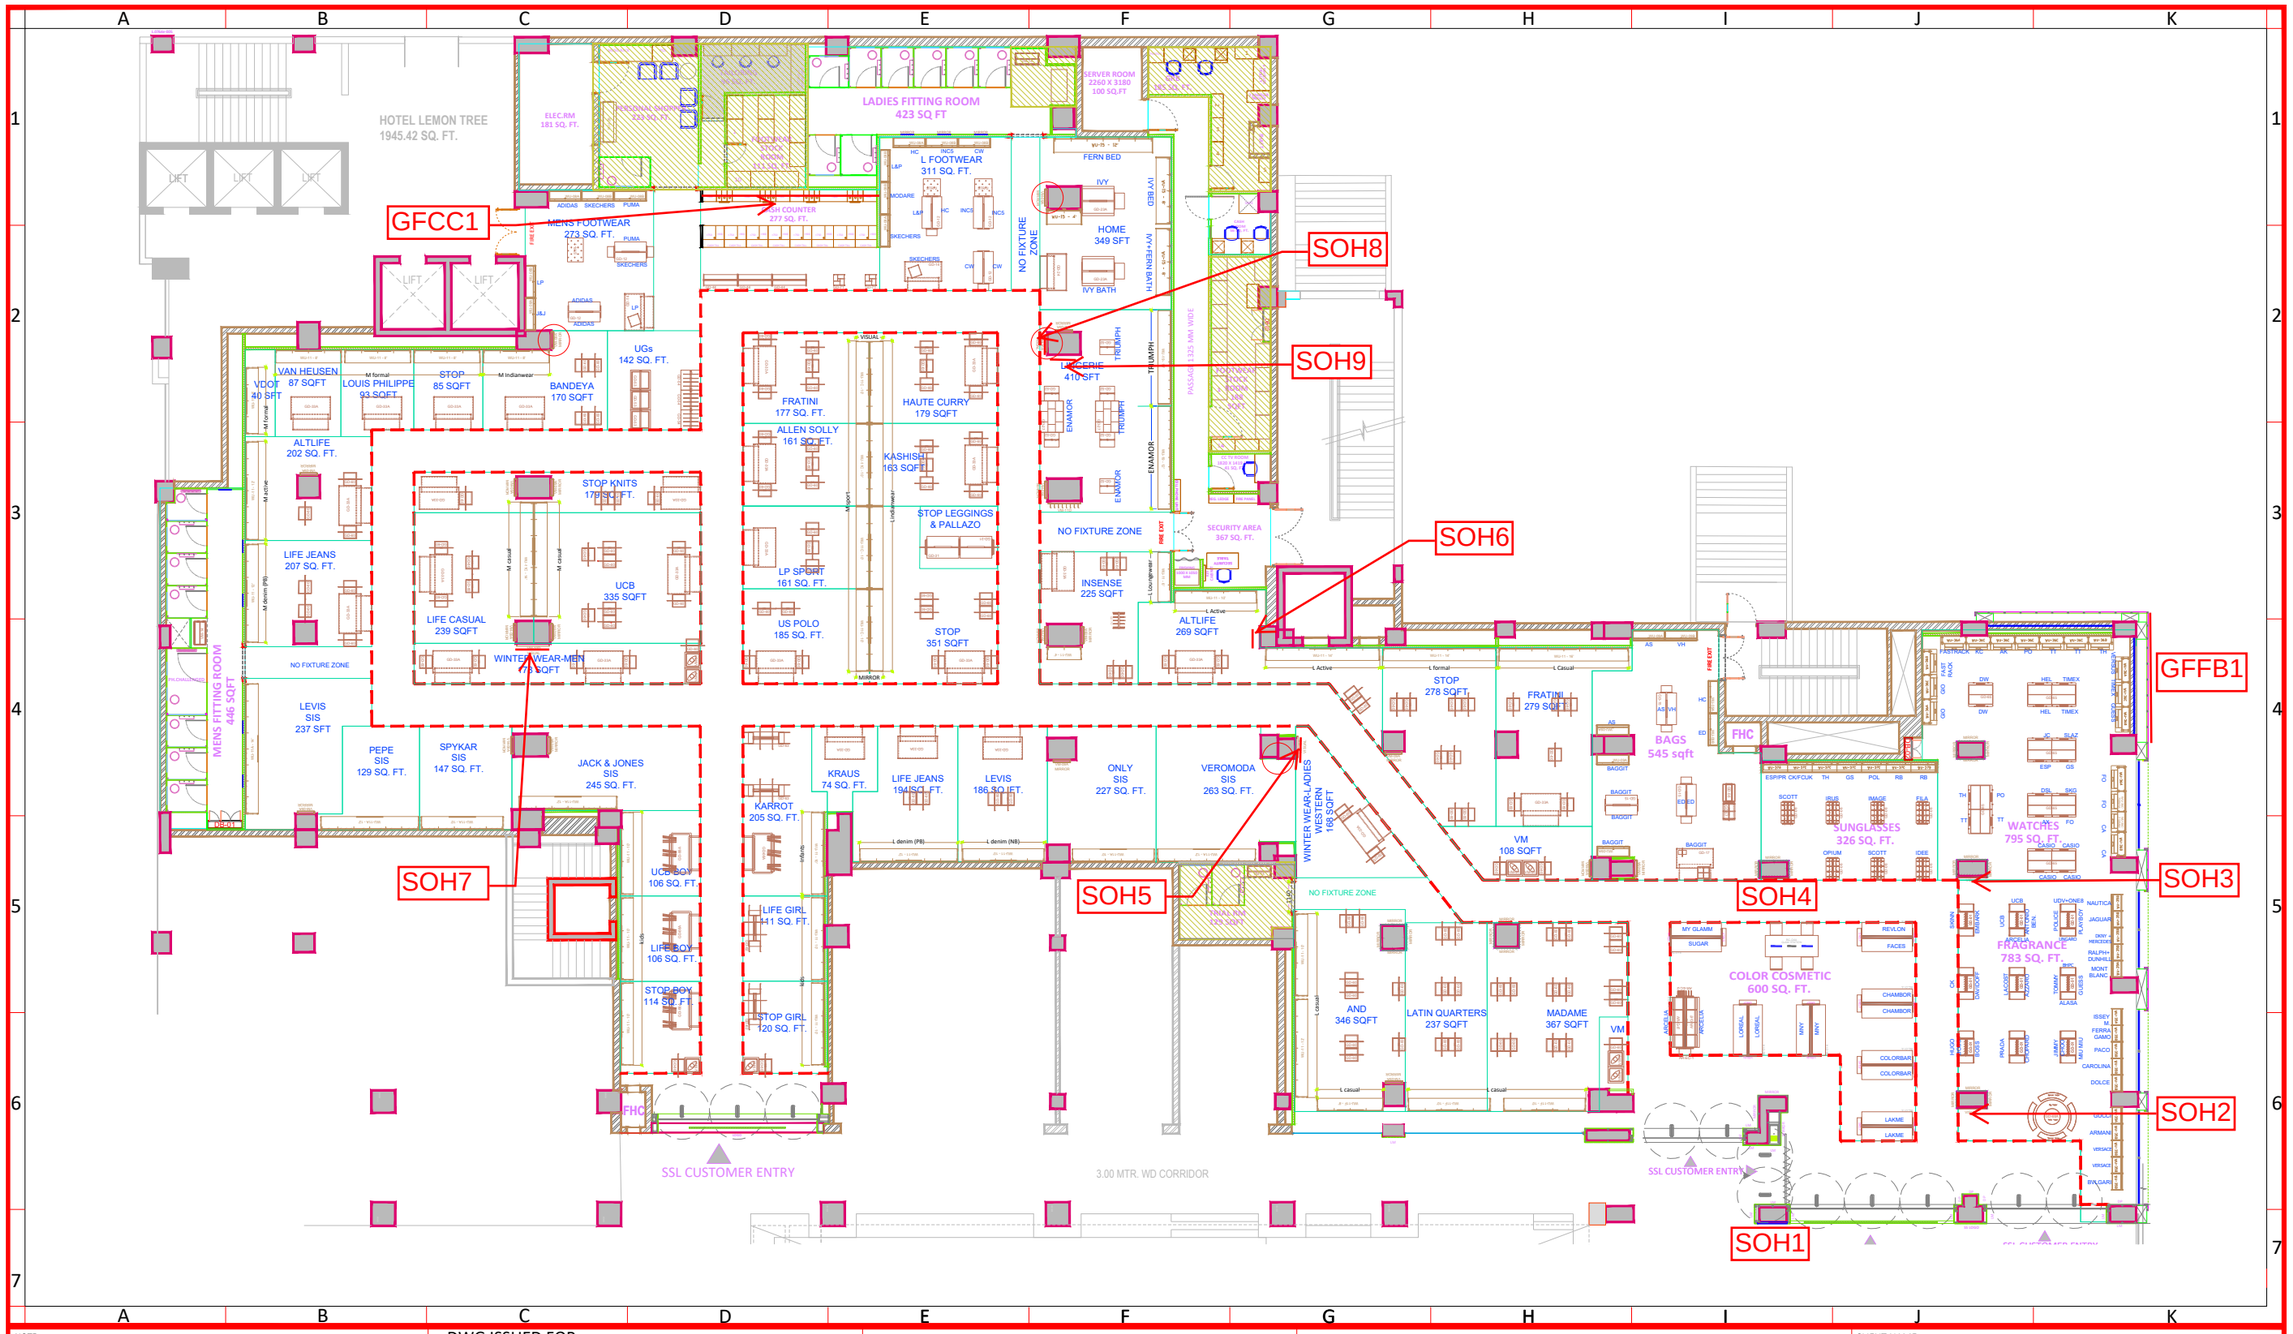

NOTE:
THIS DRAWING IS THE PROPERTY OF DESIGNOUS BUILD SOLUTIONS PVT. LTD ARCHITECTS AND INTERIOR DESIGNERS & SHALL NOT BE COPIED BY ANY ONE IN PART OR IN WHOLE WITHOUT THE PERMISSION OF THE DIRECTORS IN WRITING HAVING BEEN OBTAINED FIRST.

NOTES:

1. ALL DIMENSIONS ARE IN MM.
2. ALL LEVELS INDICATED ARE IN MM.
3. DIMENSIONS / LEVELS INDICATED ARE STRUCTURAL UNLESS OTHER SPECIFIED
4. THIS DRAWING, UNLESS OTHERWISE MENTIONED, TO BE PLOTTED TO STANDARD A4 SIZE.
5. ONLY WRITTEN DIMENSIONS TO BE FOLLOWED. DO NOT SCALE THE DRAWING
6. DIMENSIONS / LEVELS SHOWN TO BE VERIFIED AT SITE BEFORE COMMENCEMENT OF WORK ANY DISCREPANCIES IF NOTED,SHOULD BE BROUGHT TO THE NOTICE OF ARCHITECT PRIOR TO COMMENCEMENT OF WORK.
7. RELEVANT SERVICES DRAWINGS ARE TO BE READ SIMULTANEOUSLY AND PROVISION OF CUTOUTS / SLEEVES TO BE PROVIDED AS REQUIRED.
8. ALL MATERIALS / FINISHES TO BE AS SPECIFIED AND APPROVED.

DWG ISSUED FOR

TENDER	☐	APPROVAL	☐
ADVANCE COPY	☐	COMMENTS	☐
EXECUTION	■	RECORD	☐

REV NO.	DATE	DESCRIPTION	DWN.BY	CHKD.BY	APP.
R7	17.06.21	AS PER COMMENT (REVISION IN PARTITION)	BHAVANA	PRANAY	------
R6	07.06.21	AS PER COMMENT	BHAVANA	PRANAY	------
R5	19.05.21	CASH ROOM AREA ADDED	KINJAL	------	------
R4	13.05.21	AS PER CLIENT COMMENT	KINJAL	------	------
R3	17.03.21	AS PER COMMENT	BHAVANA	KINJAL	------
R2	01.03.21	AREA DEMARCATION REVISED	KINJAL	PRANAY	------
R1	25.02.21	AS PER COMMENT	KINJAL	PRANAY	------

REV NO.	DATE	DESCRIPTION	DWN.BY	CHKD.BY	APP.
R12	01.09.21	REVISED CSD/FCD AREA	KINJAL	PRANAY	---------
R11	09.08.21	REVISED AS PER SITE MEASUREMENT	KINJAL	PRANAY	---------
R10	06.08.21	REVISED AS PER SITE MEASUREMENT	BHAVANA	PRANAY	---------
R9	30.07.21	REVISED AS PER SITE MEASUREMENT	BHAVANA	PRANAY	---------
R8	14.07.21	REVISED ELEC LOCATION	KINJAL	PRANAY	---------

CLIENT NAME: SHOPPERS STOP LIMITED

PROJECT TITLE:
PROPOSED INTERIOR FITOUT FOR SHOPPERS STOP AT GROUND FLOOR 7 BASEMENT AT EAST DELHI MALL, PLOT NO. 1, GHAZIABAD, UTTAR PRADESH 201001

designous
build solutions pvt. ltd.
ARCHITECTS & INTERIOR DESIGNERS

Studio:
Ground Floor,
Balaji Infotech Park
Plot No A-278,Wagle Industrial Estate,
Road No,16-A
Thane(w)-400604
Mumbai
Board No- + 91 22 25821516
Web Site -www.designous.co.in

DRAWING TITLE:
GROUND FLOOR- FIXTURE LAYOUT

NORTH

DRAWN BY:	CHKD BY:	SCALE:	DATE:
KINJAL	PRANAY	NTS	07.09.2021

DWG NO.
JDC-20-21-299/WD/04

REVISION R12