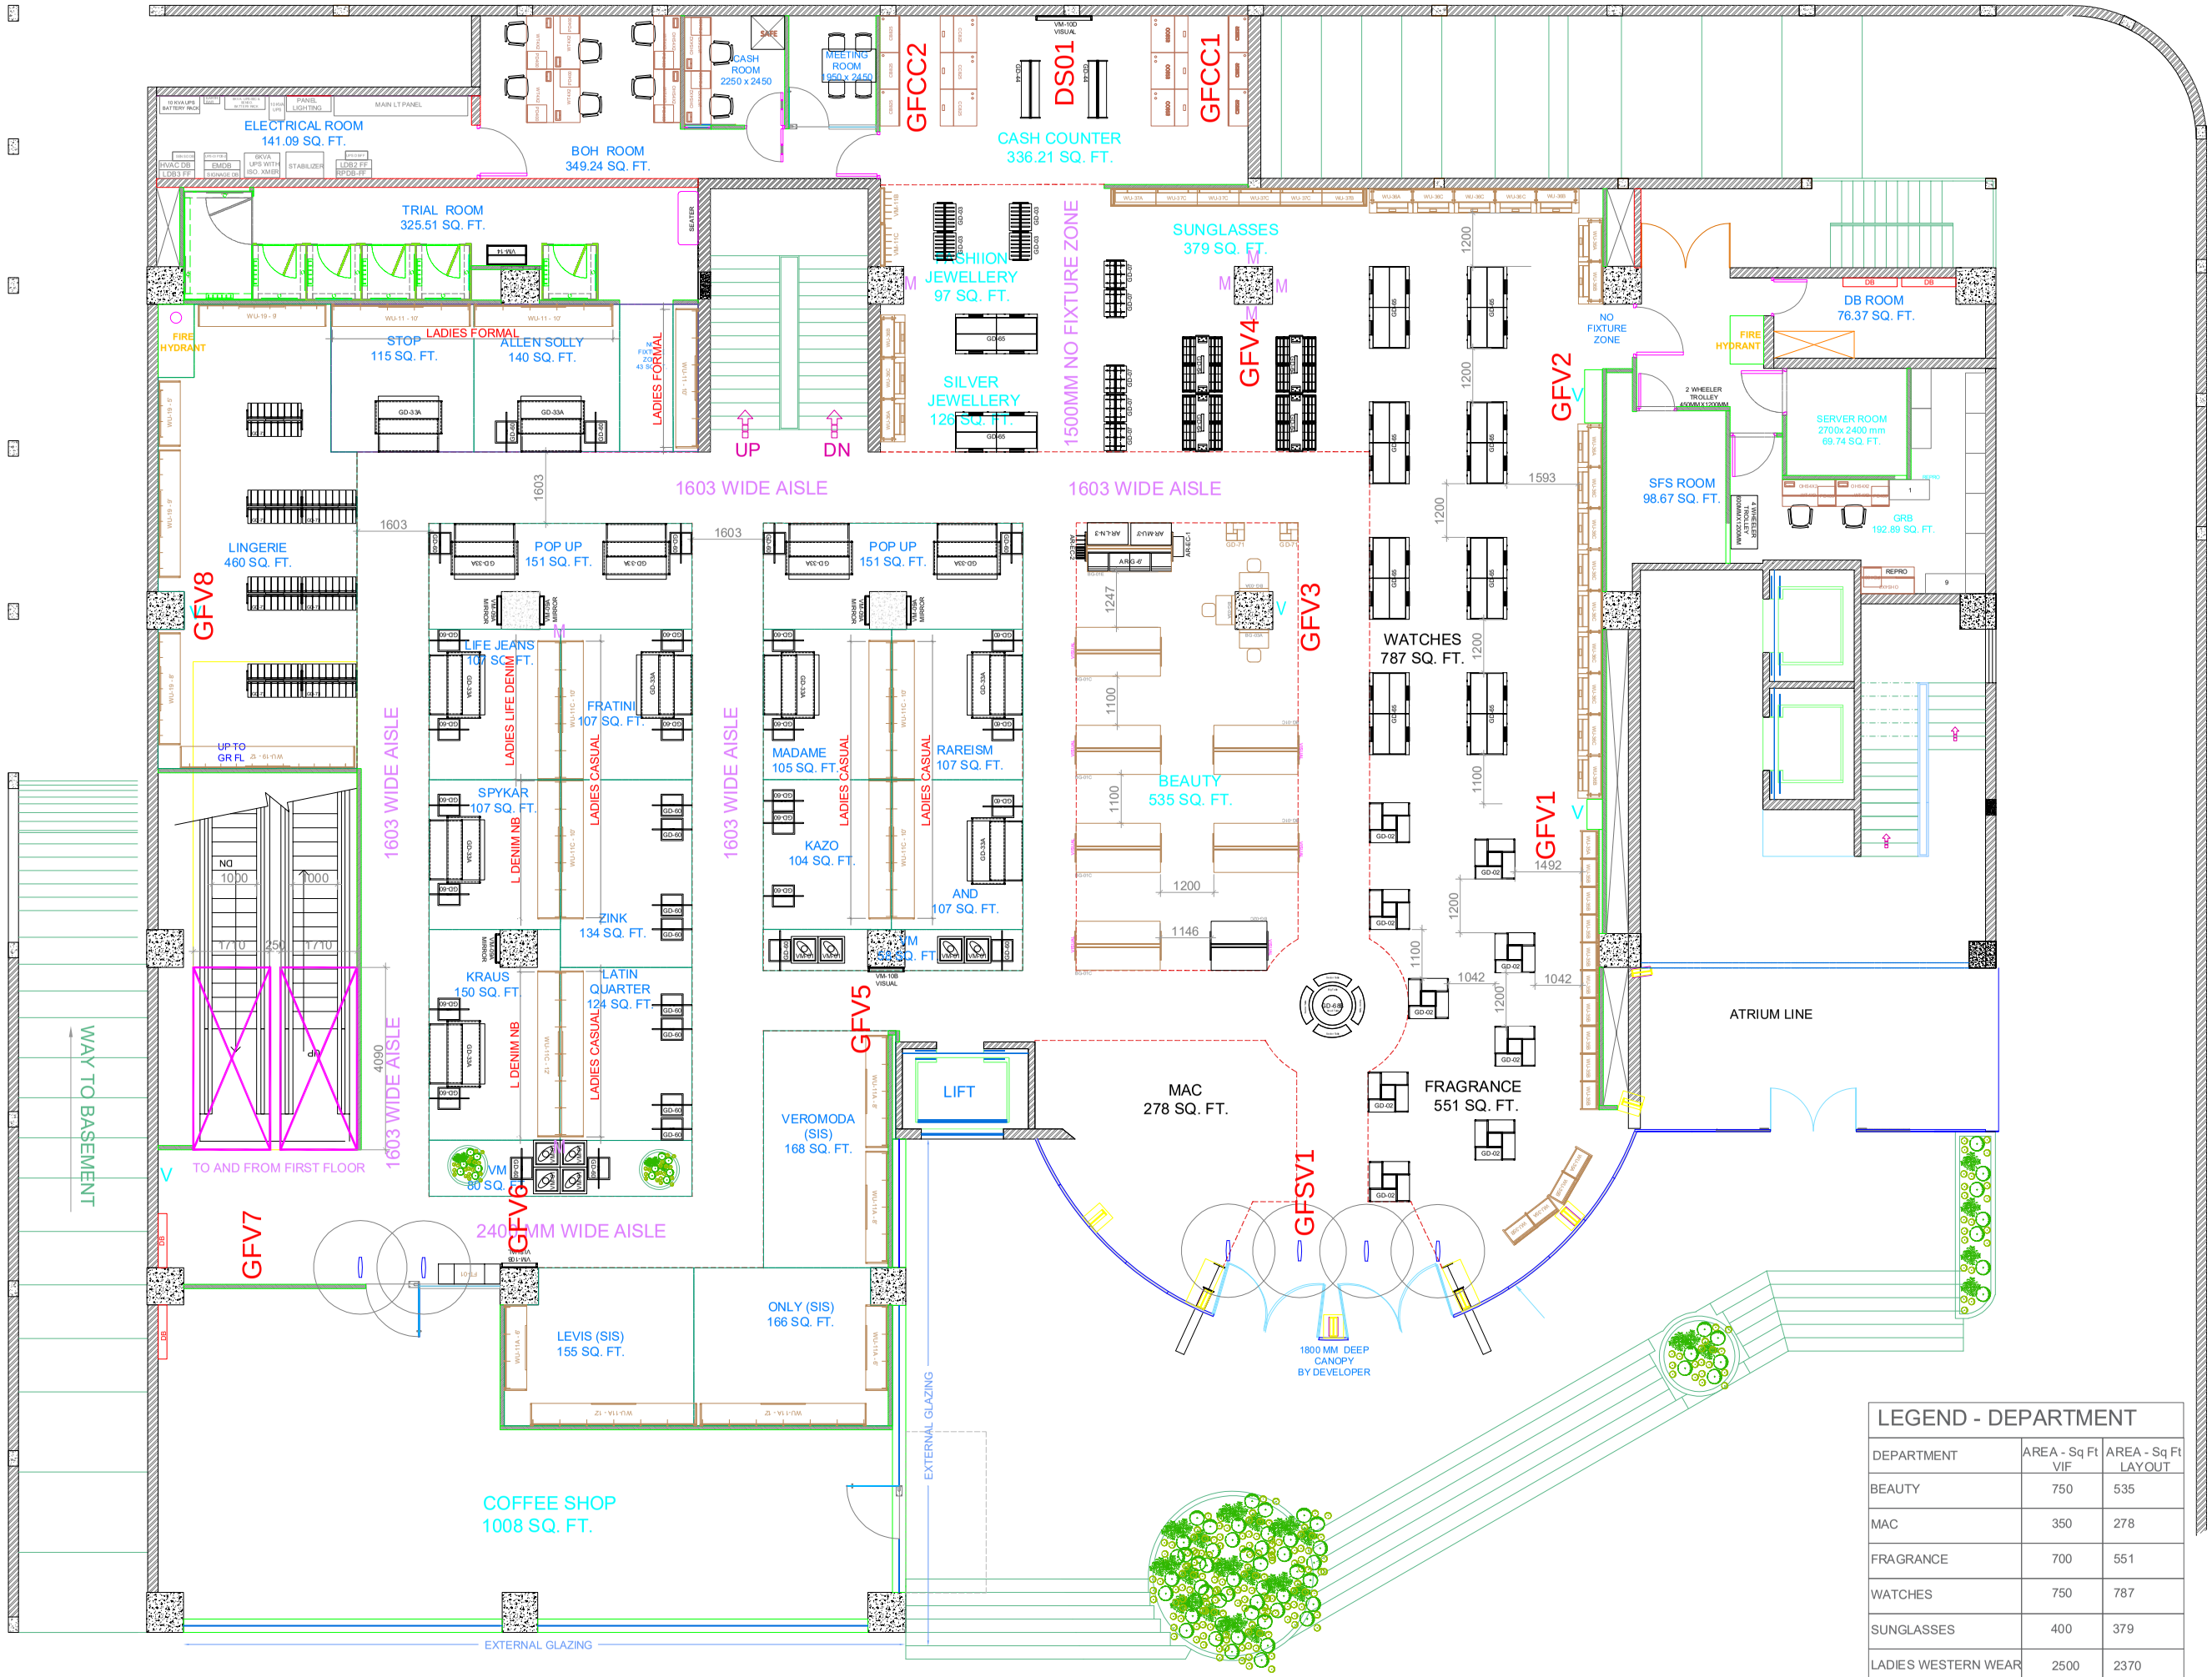

01 GROUND FLOOR
SCALE : 1:NTS

LEGEND - DEPARTMENT

DEPARTMENT	AREA - Sq Ft VIF	AREA - Sq Ft LAYOUT
BEAUTY	750	535
MAC	350	278
FRAGRANCE	700	551
WATCHES	750	787
SUNGLASSES	400	379
LADIES WESTERN WEAR	2500	2370
LINGERIE	420	466
CAFE - STARBUCKS	800	1008
CASH COUNTER		336.21

GENERAL NOTES

1. Only written dimension to be followed.
2. Any discrepancies should be referred to the architect.
3. This drawing & its copy right is the property of Studio AIRD.
4. It should not to be used, copied, traced or reproduced without their written permission.

REVISION

SR.NO.	DESCRIPTION	DATE

HVAC, PLUM. & FF CONSULTANT

ELECTRICAL CONSULTANT

CLIENT

GFC TRACKER

DATE	REV. NO.	REV. DATE

REVISION
R0

PROJECT TITLE

GUPTA TOWER NAGPUR

DRAWING TITLE

AISLE LAYOUT
GROUND FLOOR

DRAWING NO.

ISSUED FOR

☐ INFORMATION ☐ APPROVAL
☐ COMMENTS ☐ TENDER
☐ EXECUTION ☐ AS-BUILT

DATE	SHEET. NO.	SCALE
02-08-2024	-	1:100
DRAWN BY	CHECK BY	APP. BY
DIPTI	SHILPA	SATISH

FOR NORTH DIRECTION, PLEASE REFER SITE PLAN FOR ORIENTATION OF BUILDING

STUDIO AIRD
ARCHITECTURE • INTERIOR DESIGN • RETAIL DESIGN
Fairlink Center, A-703/706,Off New link Road
Andheri West, Mumbai, Maharashtra 400053