


ZONE SOUTH STORE CODE 158

STORE NAME VIJAYWADA CARPET AREA 48,336 SQ.FT

FLOOR GROUND FLOOR SEASON AW 22 AW22 Layout Okay for Re-Release Neeraj Jagga 12.08.2022

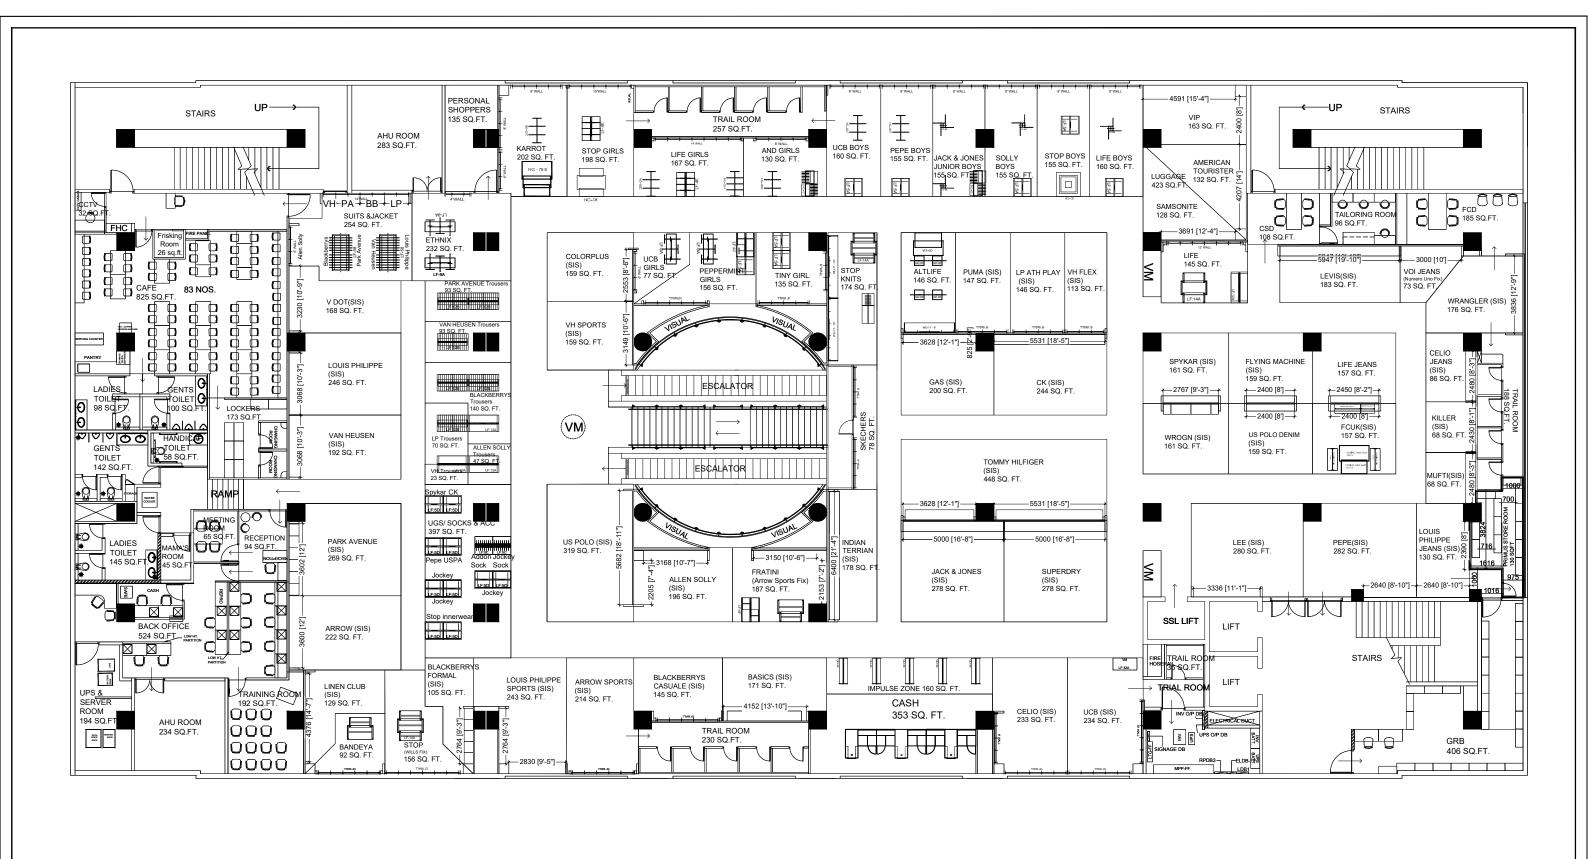

ZONE SOUTH STORE CODE 158

STORE NAME VIJAYWADA CARPET AREA 48,336 SQ.FT

FLOOR FIRST FLOOR SEASON AW 22 AW22 Layout
Okay for
Re-Release
Neeraj Jagga
12.08.2022